

[illegible]

R.CONC. ROOF SLAB AS PER ENG. DESIGN WITH MIN 30mm SCREED AT 1:50 FALL TO OUTLETS WITH "DERBIGUM" TORCH-ON WATERPROOFING (APPLIED STRICTLY TO MANUFACTURER'S SPECIFICATIONS. INSTALL ONE 50mm LAYER OF 19-22mm STONE AGGREGATE ON TOP OF GEOTEXTILE, ON 50mm ISOBOARD INSULATION, OR "DELTA MS-8" DIMPLED DRAINAGE LAYER. ALL TO MANUFACTURER'S SPECIFICATION.

SOLAR PANEL
COLLECTOR ON ROOF

2

ROOF PLAN

1 : 100

R.CONC. ROOF SLAB AS PER ENG. DESIGN WITH MIN 300mm SCREED AT 1:50 FALL TO OUTLETS WITH "BERIBUM" TORCH-ON WATERPROOFING (APPLIED STRICTLY TO MANUFACTURER'S SPECIFICATIONS).
INSTALL ONE 50mm LAYER OF 19-22mm STONE AGGREGATE ON TOP OF GEOTEXTILE, ON 50mm ISOBOARD INSULATION, ON "DELTA MS-8" DIMPLED DRAINAGE LAYER. ALL TO MANUFACTURER'S SPECIFICATION.

GENERAL NOTES

ALL MEASUREMENTS, HEIGHT AND DESCRIPTIONS MUST BE CHECKED ON THE PLAN BEFORE COMMENCEMENT OF ANY WORK ON SITE. ANY DISCREPANCIES, FAULTS IDENTIFIED, ARE TO BE COMMUNICATED WITH THE ARCHITECT. COPYRIGHTS IN THIS DESIGN AND DRAWINGS IS RESERVED TO THE ARCHITECT. TAKE NOTE THAT WHERE A SPECIFIC MANUFACTURE NAME IS USED THE WORKSMANMUST BE CORRECT TO THE SPECIFICATION OR IF OTHERWISE ALTERATION/DEVIATION TO BE CONSULTED WITH THE ARCHITECT. THE CONTRACTOR/BUYER TO FAMILIARISE HIMSELF WITH THE SPECIFICATIONS OF ANY SPECIFIED MANUFACTURER.

SITE LAYOUT

THE CONTRACTOR/BUYER TO FAMILIARISE THEMSELVES WITH THE LAYOUT, MEASUREMENTS, AND ALL ADDITIONAL ANNOTATION WITH REGARDS TO THE FOOTPRINT OF THE STRUCTURE ON SITE. ANY ELECTRICAL, SEWERAGE, STORMWATER SERVICE TO BE CONSIDERED BEFORE ANY WORK COMMENCES ON SITE. ANY CHANGED TO SUCH RESERVATIONS ARE THE RESPONSIBILITY OF THE OWNER. THE ENGINEER WILL BE RESPONSIBLE FOR ANY CLASH, LOAD BEARING STRUCTURES AND DEFECTIVE/SENSITIVE/IRREGULAR GROUND CONDITIONS

CHIMNEYS AND BRAIRS

VERIFICATION OF CORRECT SIZES TO BE CONSIDERED AS PER MANUFACTURES DETAILS BEFORE ANY CHIMNEY/ BRAIR ARE BUILT. ANY DEVIATION FROM THE PROPOSED STRUCTURES TO DISCREPANCY WITH THE ARCHITECT BEFORE HAND.

ELECTRICAL

REFER TO ELECTRICAL PLAN AND MUST BE DISCUSSED WITH CLIENTS BEFORE HAND. INDICATION OF ANY GARDEN LIGHTS AND REMOTE GATE CONTROLS NOT SHOWN ON THE PLAN.

FOUNDATION

FOUNDATION DESIGNS TO COMPLY WITH SANS 10400-B OR THE DETALLED REQUIREMENTS OF SANS 10400-H. RECOMMENDATIONS AND PREFERRED FOUNDATION METHODS TO BE CONFIRMED WITH THE APPOINTED ENGINEER PRIOR TO ANY COMMENCEMENT OF ANY GROUND WORKS.

WALLS

CONSTRUCTION OF WALLS TO COMPLY WITH THE SANS 10400-B & 10400-T. A STANDARD (Ø 220mm) EXTERNAL WALL & 110mm to be applied. STRENGTH AND STABILITY ON ALL WALLS ARE REQUIRED IN CONJUNCTION WITH STANDARD BUILDING PRACTICE. WALL FINISHES TO COMPLY WITH THE SPECIFICATIONS ON THE ELEVATIONS.

ROOFS

ROOF COVERING AND WATERPROOFING NEED TO BE IN CONJUNCTIONS WITH THE SANS 10400-L. FLAT ROOFS OR RELATED TYPES NEED TO BE IN CONJUNCTION IN ACCORDANCE WITH THE DETAILED REQUIREMENTS OF SANS 10400-L OR RATIONALLY DESIGNED BY AN APPROVED COMPETENT PERSON. ROOF ASSEMBLY AND CEILING INSTALLATION MUST BE CONSTRUCTED IN ACCORDANCE WITH THE SANS 10400-L AS WELL AS SANS 10400-I & 10400-O OR SANS 10400-T IN TERMS OF THE FIRE RESISTANCE & COMBUSTIBILITY. GUTTERS & DOWNPIPS MUST BE SIZED IN ACCORDANCE WITH SANS-10400-M

LIGHTING AND VENTILATION

CROSS VENTILATION (5%) AND LIGHTING (10%) IN HABITABLE ROOMS. LIGHTING AND VENTILATION IN ANY ROOM SHOULD COMPLY WITH SANS 10400-T AND THE REQUIREMENTS OF SANS 10400-O OR ALTERNATIVELY TO BE RATIONALLY DESIGNED. MECHANICAL VENTILATION AND ARTIFICIAL LIGHTING TO BE CONSIDERED FOR BASEMENTS AND ROOMS ALIKE.

DRAINAGE DRAINAGE SYSTEMS TO BE IN ACCORDANCE WITH SANS 10400-P OR ALTERNATIVELY RATIONALLY DESIGNED BY A COMPETENT PERSON. THE FOLLOWING TO BE CONSIDERED WITH THE INSTALLATION OF THE DRAINAGE SYSTEM:
--

- WC TO BE FITTED TO 110mm DIA uPVC SOIL PIPE
- HWB/SINKS/BATHS/SHOWERS
TO BE FITTED TO 50mm DIA uPVC WASTE PIPE

DRAINAGE INVERT LEVEL TO BE A MINIMUM OF 450MM.
ALL SOIL PIPES BE INSTALLED USING UPVC 100MM DIA PIPES WITH A STANDARD GRADIENT OF 1:40. THE GRADIENT TO BE CONSIDERED AS PER SLOPE OF FALL ON THE SITE AS PROVISIONS TO BE MADE DEPENDANT ON THE SURFACE

FIRE NOTES
INSTALLATION TO BE DONE ACCORDING TO THE T TO THE SANS 10400 - W AND WATER SUPPLY ACCORDING TO SANS 10400-T OR AS PER RATIONAL DESIGN BY COMPETENT PERSON. -ALL CHIMNEYS AS PER PART "v" OF NBR -NO COMBUSTIBLE ROOF ELEMENTS SHALL PENETRATE THE SEPARATING ELEMENTS BETWEEN ANY HABITABLE ROOM AND GARAGE. -ALL DOORS LEADING TO THE GARAGE TO BE SOLID WOOD STABLE DOORS, FOR FIREPROOF DOOR TYPE.

STORM WATER
IMPLEMENTED ACCORDING TO SANS 10400-R OR RATIONALLY DESIGNED BY AN APPROVED COMPETENT PERSON.

GLAZING
THE TYPE AND FIXING TO BE IN ACCORDANCE WITH SANS 10400-B OR THE DETAILED REQUIREMENTS OF SANS 10400-N. GLAZING SELECTION TO BE MADE IN ACCORDANCE TO THE DETAILED REQUIREMENTS OF SANS 10400-N. SEE NOTES ON ALL SELECTION ON THE WINDOW SCHEDULE.

-GLAZING AS PER "N" OF NBR

STAIR DETAIL
STAIRWAYS TO F CONSTRUCTED IN ACCORDANCE TO THE SANS 10400-B & SANS 10400-T OR DETAILED REQUIREMENTS OF SANS 10400-M. A COMPETENT PERSON TO BE APPOINTED WITH REGARDS TO THE STABILITY AND STRENGTH OF THE STAIRWAYS. ANY ITEM(S) ACTING AS BALUSTRADES TO THE STAIRS NEED TO COMPLY WITH SANS 10400-B &/OR SANS 10400-K &/OR 10400-T.

STAIRWAY:
TREADS - MIN 250MM
RISERS - MAX 200MM
FLOOR FINNISH TO BE CARPET OR SLIP-FREE TILES AS CHOSEN BY CLIENT.

BALUSTRADES:
-MIN 1000MM HIGH BALUSTRADES STEEL/GLASS/ALUMINUM AS CHOSEN BY CLIENT.
-100MM SPACING
-SPECIFICATION AS PER MANUFACTURER
-ENGINEER DETAILS FLS EWHRE

PROJECT TITLE	PROPOSED NEW DWELLING FOR: SS DE BEER ON STAND : 1103 EERSTERUST X02
---------------	--

OWNERS NAME SS DE BEER	OWNERS SIGNATURE 
---------------------------	---

ENGINEER NAME AND No:	ENGINEER SIGNATURE:
-----------------------	---------------------

PREPARED BY:	ARCHITECT:

KLK	LJW

SACAP REG: CAD54585565	SACAP REG: 5838
------------------------	-----------------

SIGNATURE: _____

	27/02/2024
--	------------

 **RESO PROJECTS (PTY) LTD**
*BLOCK A, ERASMUS FORUM
274 STOKKIESDRAAI AVE
ERASMUSRAND*
079 516 6804
resoprojects@outlook.com

DRAWING TITLE:
SITE PLAN, FLOOR PLAN, SECTIONS, ELEVATION & SCHEDULES

Circumstance	Percentage of respondents who believe that the use of force is justified in the circumstance
All circumstances	85%
Only in self-defense	15%
Only in defense of others	0%
Only in defense of property	0%
Only in defense of a law	0%
Only in defense of a person	0%
Only in defense of a group	0%
Only in defense of a community	0%
Only in defense of a nation	0%
Only in defense of the world	0%

DATE:	2023/03/30	SCALE:	As indicated	SHEET SIZE:	A1
-------	------------	--------	--------------	-------------	----

PROJECT No	DRAWING No	REVISION No
------------	------------	-------------

2023-D014	000	
-----------	-----	--

[illegible]

AREA SCHEDULE	
NAME	AREA
GROUND FLOOR UFL	
COVERED ENTRANCE PATIO	2.66 m ²
COVERED PATIO	13.06 m ²
GARAGE	50.53 m ²
GROUND FLOOR	138.74 m ²
GROUND FLOOR UFL	204.99 m ²
FIRST FLOOR UFL	
COVERED BALCONY	15.00 m ²
FIRST FLOOR	153.64 m ²
FIRST FLOOR UFL	168.64 m ²
GRAND TOTAL	373.63 m ²

COVERAGE CALCULATION EXCLUSIONS:

AS PER CONDITION 4 OF CLAUSE 27: COVERAGE WITHIN THE
TSHWANE TOWN PLANNING SCHEME 2024

a.	THE BASEMENT FLOOR AREA
b.	MINOR BUILDING WORKS AS DEFINED IN THE MBR. UP TO A MINOR MAXIMUM OF 40m ² FOR ALL SUCH MINOR BUILDING WORKS ON A PROPERTY.
c.	CANOPIES OR EAVES PROJECTIONS OR ROOF OVERHANGS UP TO A MAXIMUM OF ONE (1) METRE
d.	MEASURED HORIZONTALLY FROM THE EXTERIOR WALL;
e.	THE ESCAPES
f.	LAUNDRY AREAS AND PATIOS (MORE THAN 50% OPEN WITH LOUVERS);
g.	MUNICIPAL AND OTHER SUBSTATIONS;
h.	EAVES PROJECTIONS USED EXCLUSIVELY FOR THE MAINTENANCE OF A BUILDING.
i.	SUN AND RAIN PROTECTION PURPOSES OF PEDESTRIANS ON GROUND LEVEL.
j.	RUBBISH BIN ROOMS;
k.	ANY OVER FUEL PUMPS AT FILLING STATIONS OR PUBLIC GARAGES;
l.	ANY CAR SHELTER, SUCH AS SHADE NETTING, WITH AT LEAST THREE (3) OPEN SIDES (WHICH IS NOT INCLUDED IN SUB-CLAUSE 37(b)) AND WHICH IS REQUIRED IN TERMS OF TABLES 6 AND 7, AND ANNEXURE L, CONSENT USE OR PERMISSION, PROVIDED THAT


THE NUMBER AND EXTENT, SITING AND APPEARANCE THEREOF, SHALL BE SUBJECT TO CLAUSE 31: EXCLUDING RESIDENTIAL 1. AND RESIDENTIAL 5. A.

THE MUNICIPALITY MAY IMPOSE ANY FURTHER CONDITIONS IT MAY DEEM FIT.


DEVELOPMENTAL CONTROLS									
PROPERTY DESC.:		1/1103 EERSTERUST X02			SITE AREA:		348m ²		
ZONING USE :		RESIDENTIAL 1			MIN ERF SIZE:		200m ²		
UNITS PER HA :		N/A			ANNEXURE NO.:		N/A		
		PERMISSIBLE				PROPOSED			
BUILDING LINE	STREET	NORTHERN SIDE (AS PER SCHEDULE 11)			NORTHERN SIDE				
		3M			3,15M				
	SIDE/ REAR	WESTERN SIDE		EASTERN SIDE		WESTERN SIDE		EASTERN SIDE	
		1M		1M		0M		2,09M	
	SOUTHERN BOUNDARIES	GROUND FLOOR		FIRST FLOOR		GROUND FLOOR		FIRST FLOOR	
		2M		3M		1,22M		1,22M	
COVERAGE (GF vs SITE)		50%			58.90% ((204.99/348)*100)				
COVERAGE (FF vs GF)		N/A			82.26% ((168.64/204.99)*100)				
F.A.R		N/A			N/A				
HEIGHT		10 METERS			8.16M				
DENSITY		N/A			N/A				
PARKING		N/A			N/A				
SYNOPSIS:		N/A							
CALCULATIONS	NFA CALCULATION	MAIN DWELLING	NFA = (GFA - D)*(100% - Y) = (373.63 - 0)*(95%) = 373.63*(95%) = 354.94m²		TOTAL OUT BUILDINGS	N/A		HABIT OUT BUILDINGS	N/A
	MAIN DWELLING VS OUTBUILDINGS:		HABITABLE OUTBUILDINGS			TOTAL OUTBUILDINGS			
	N/A		N/A						




1 NORTHERN ELEVATION
1 : 100

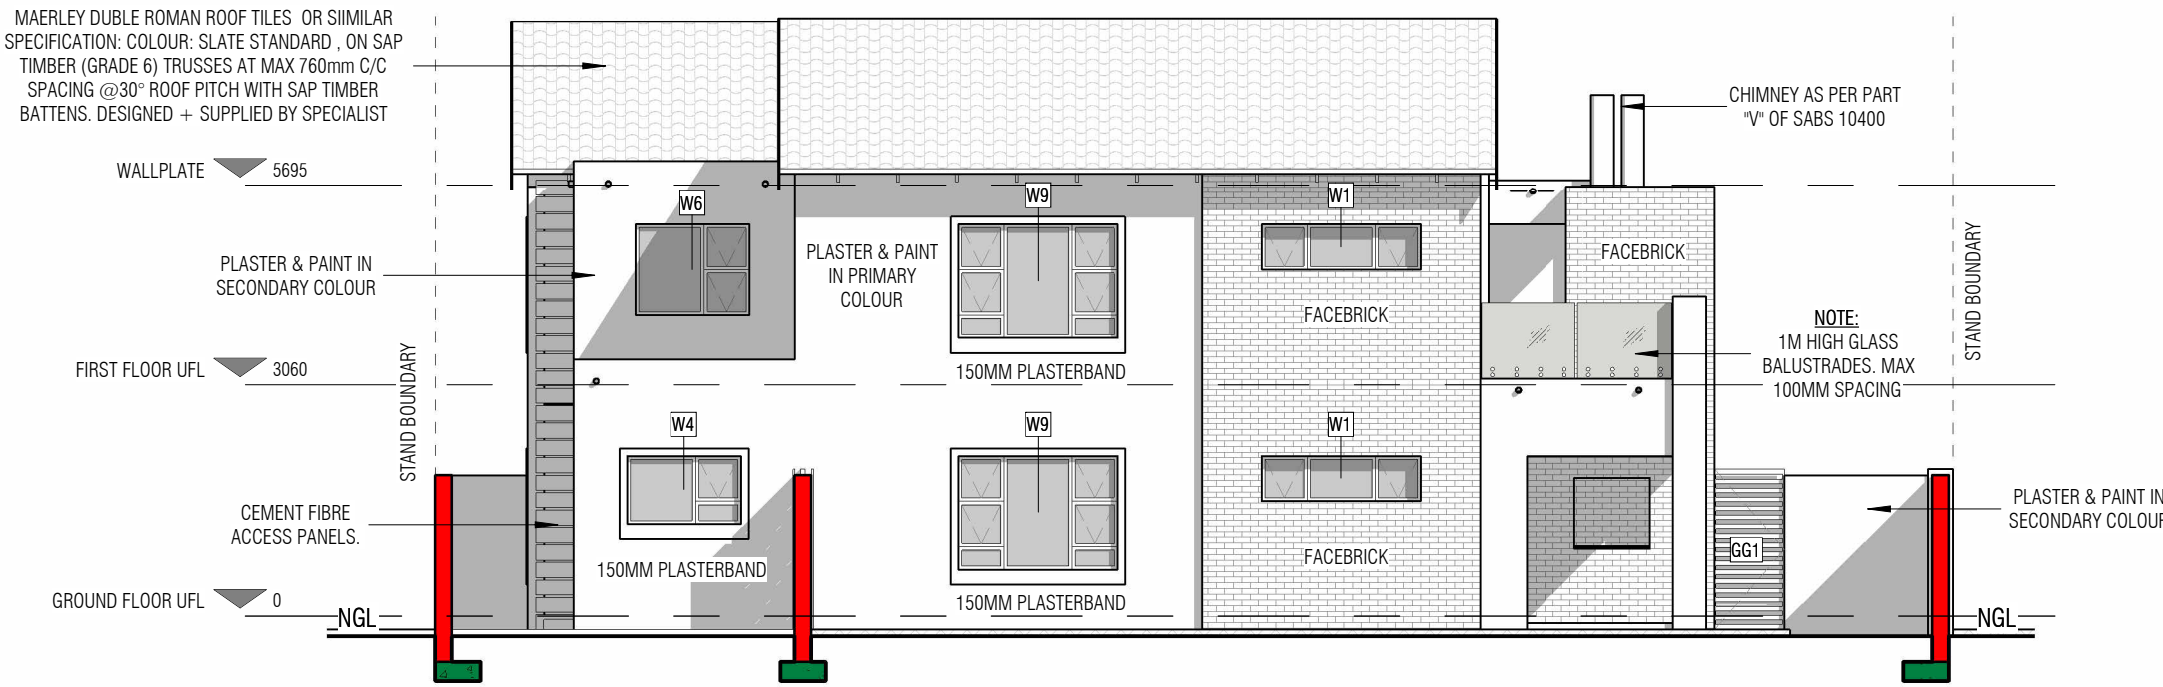


2 EASTERN ELEVATION
1 : 100

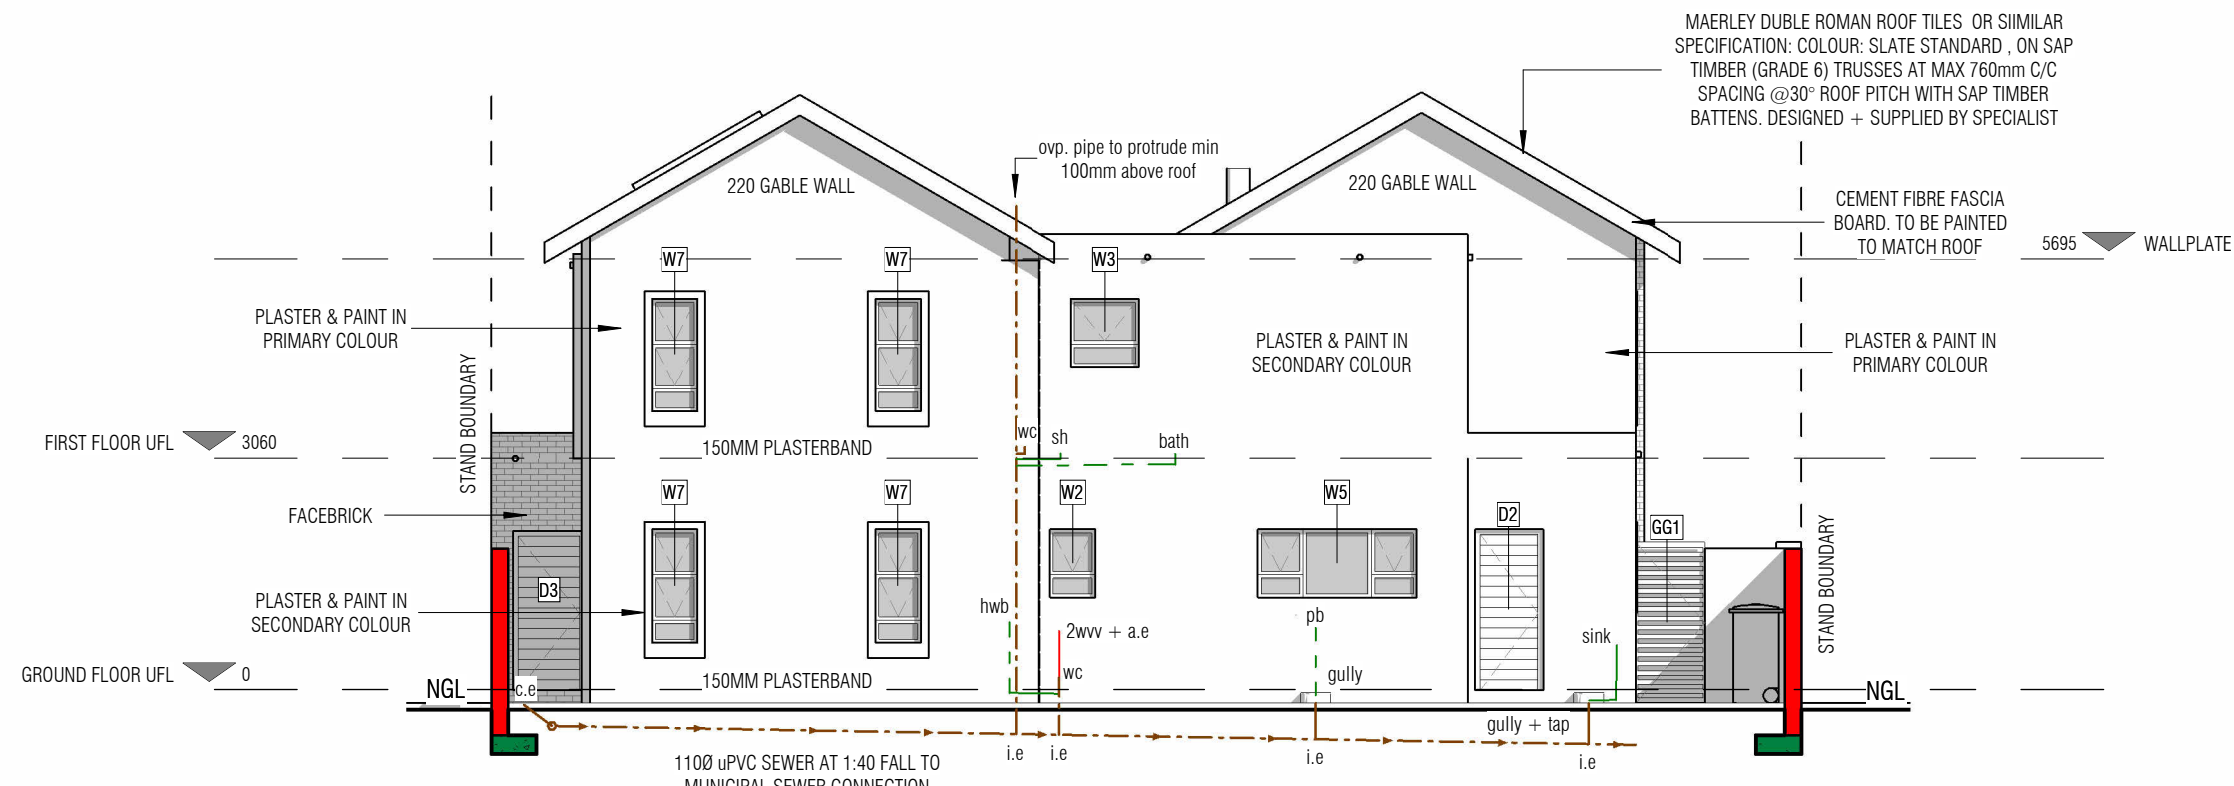


3 SOUTHERN ELEVATION
1 : 100

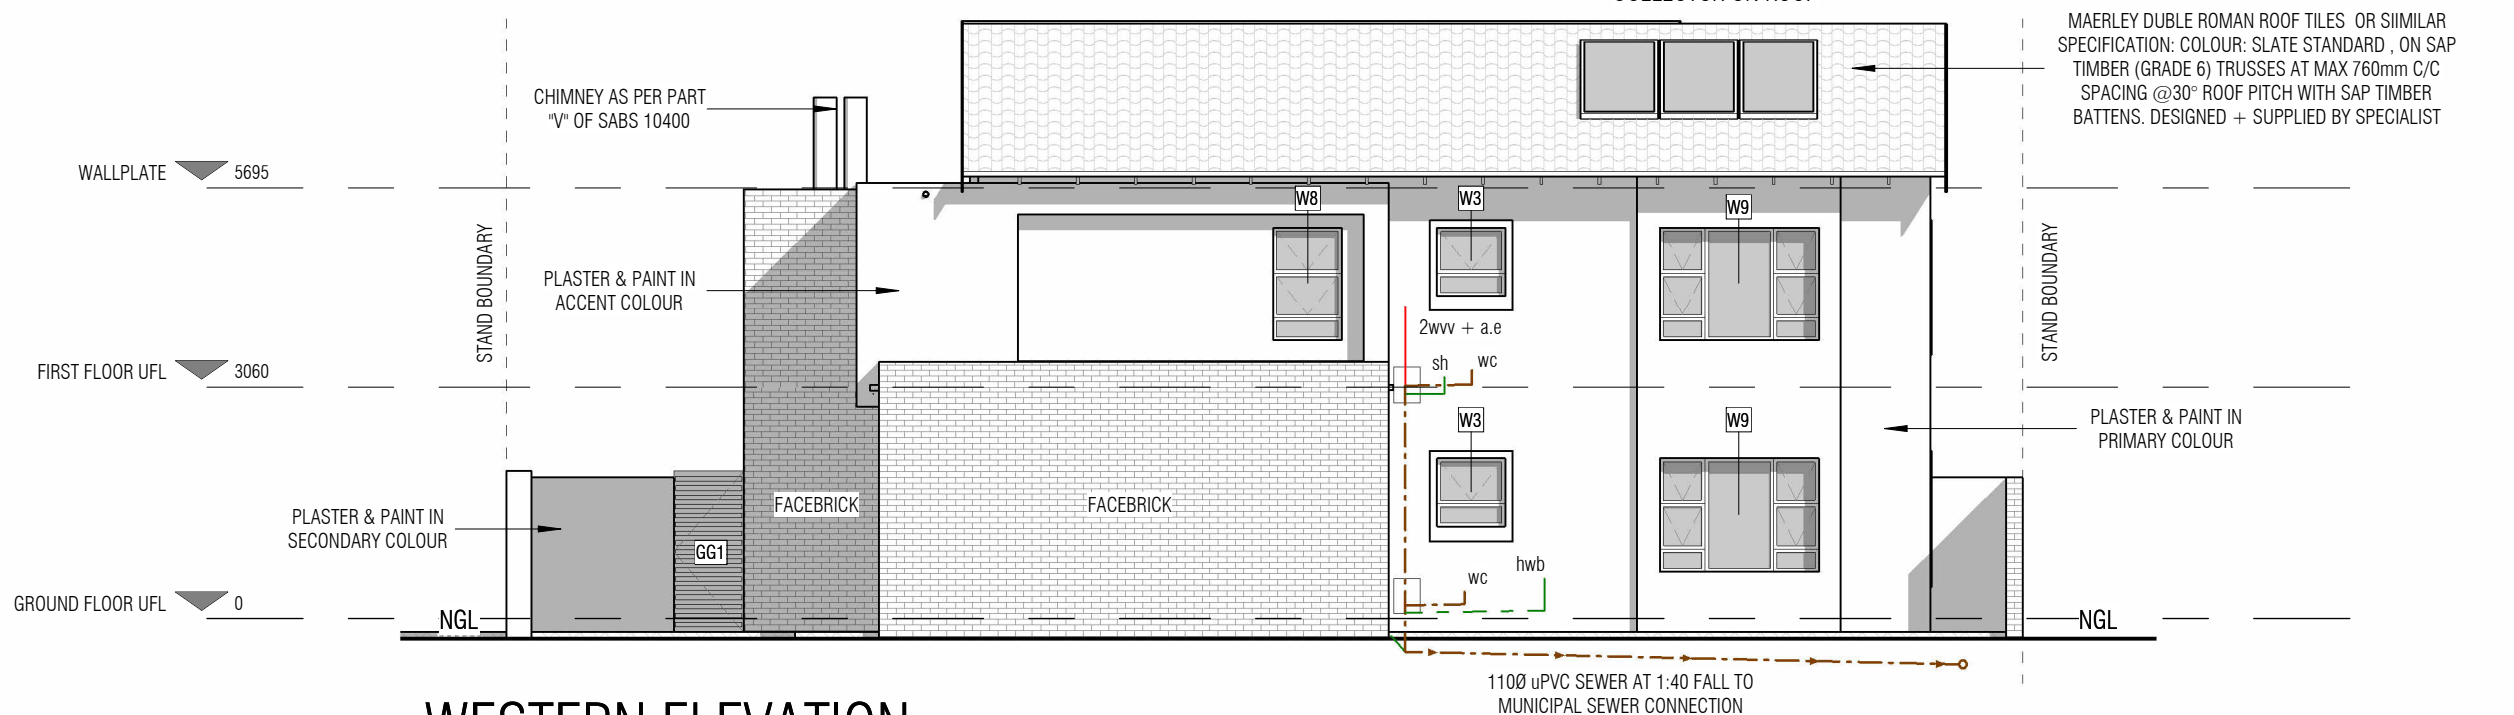


4 WESTERN ELEVATION
1 : 100

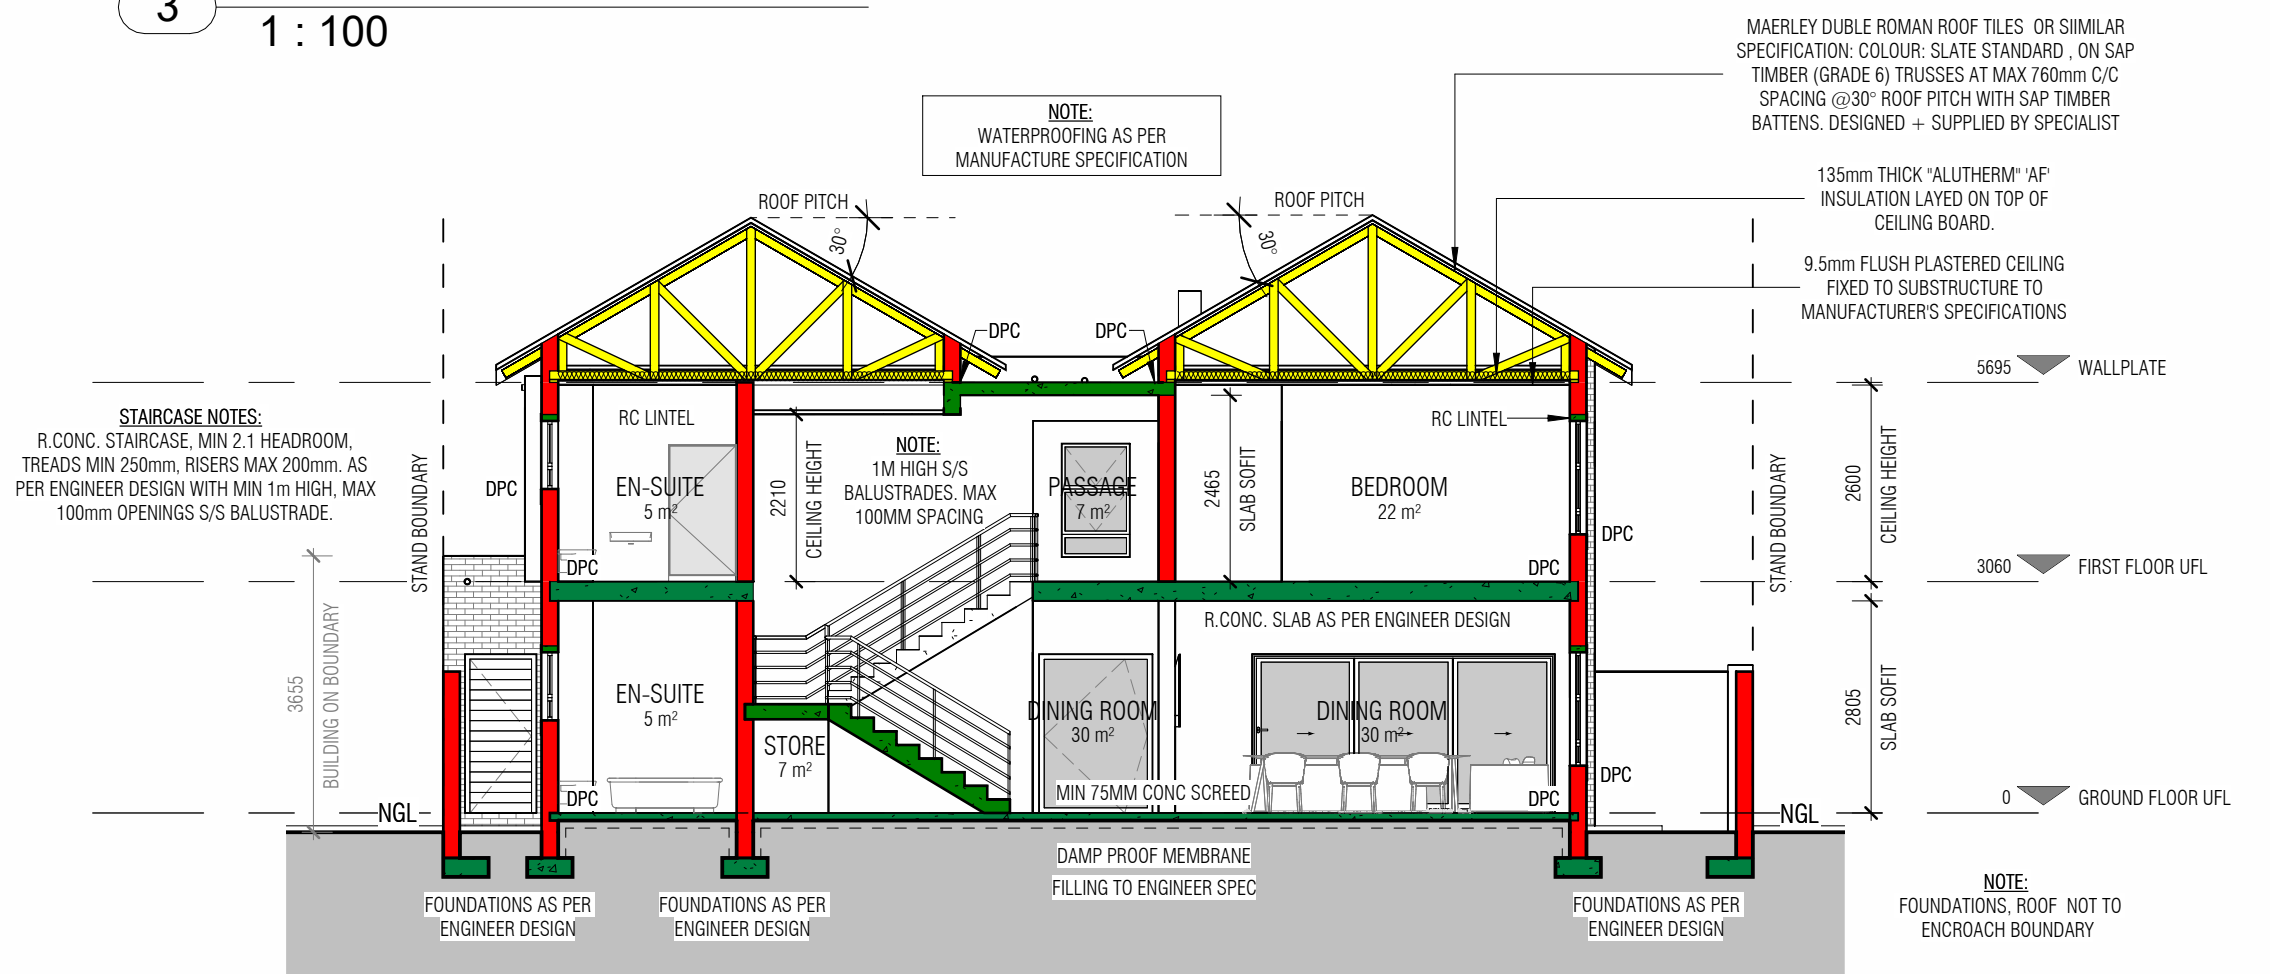

A SECTION A-A
1 : 100

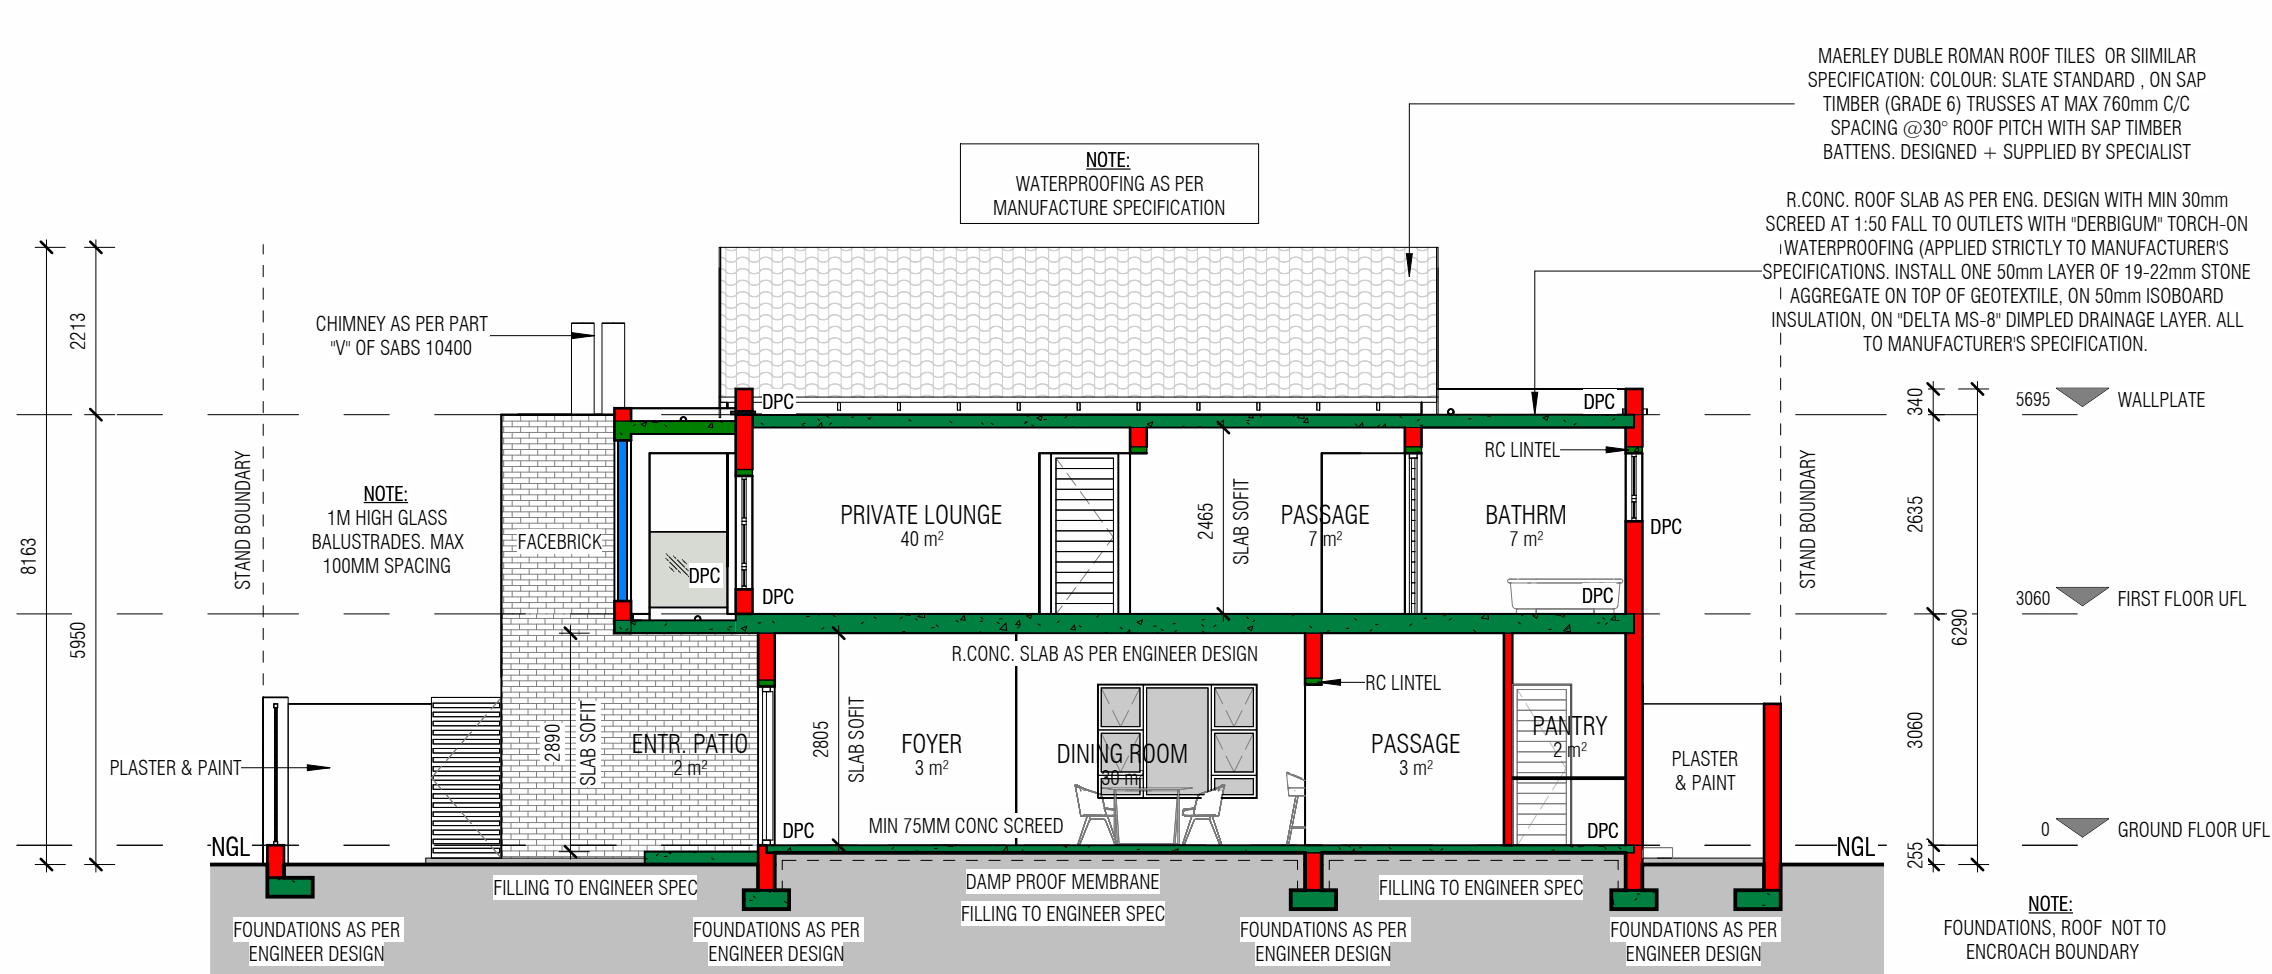

B SECTION B-B
1 : 100

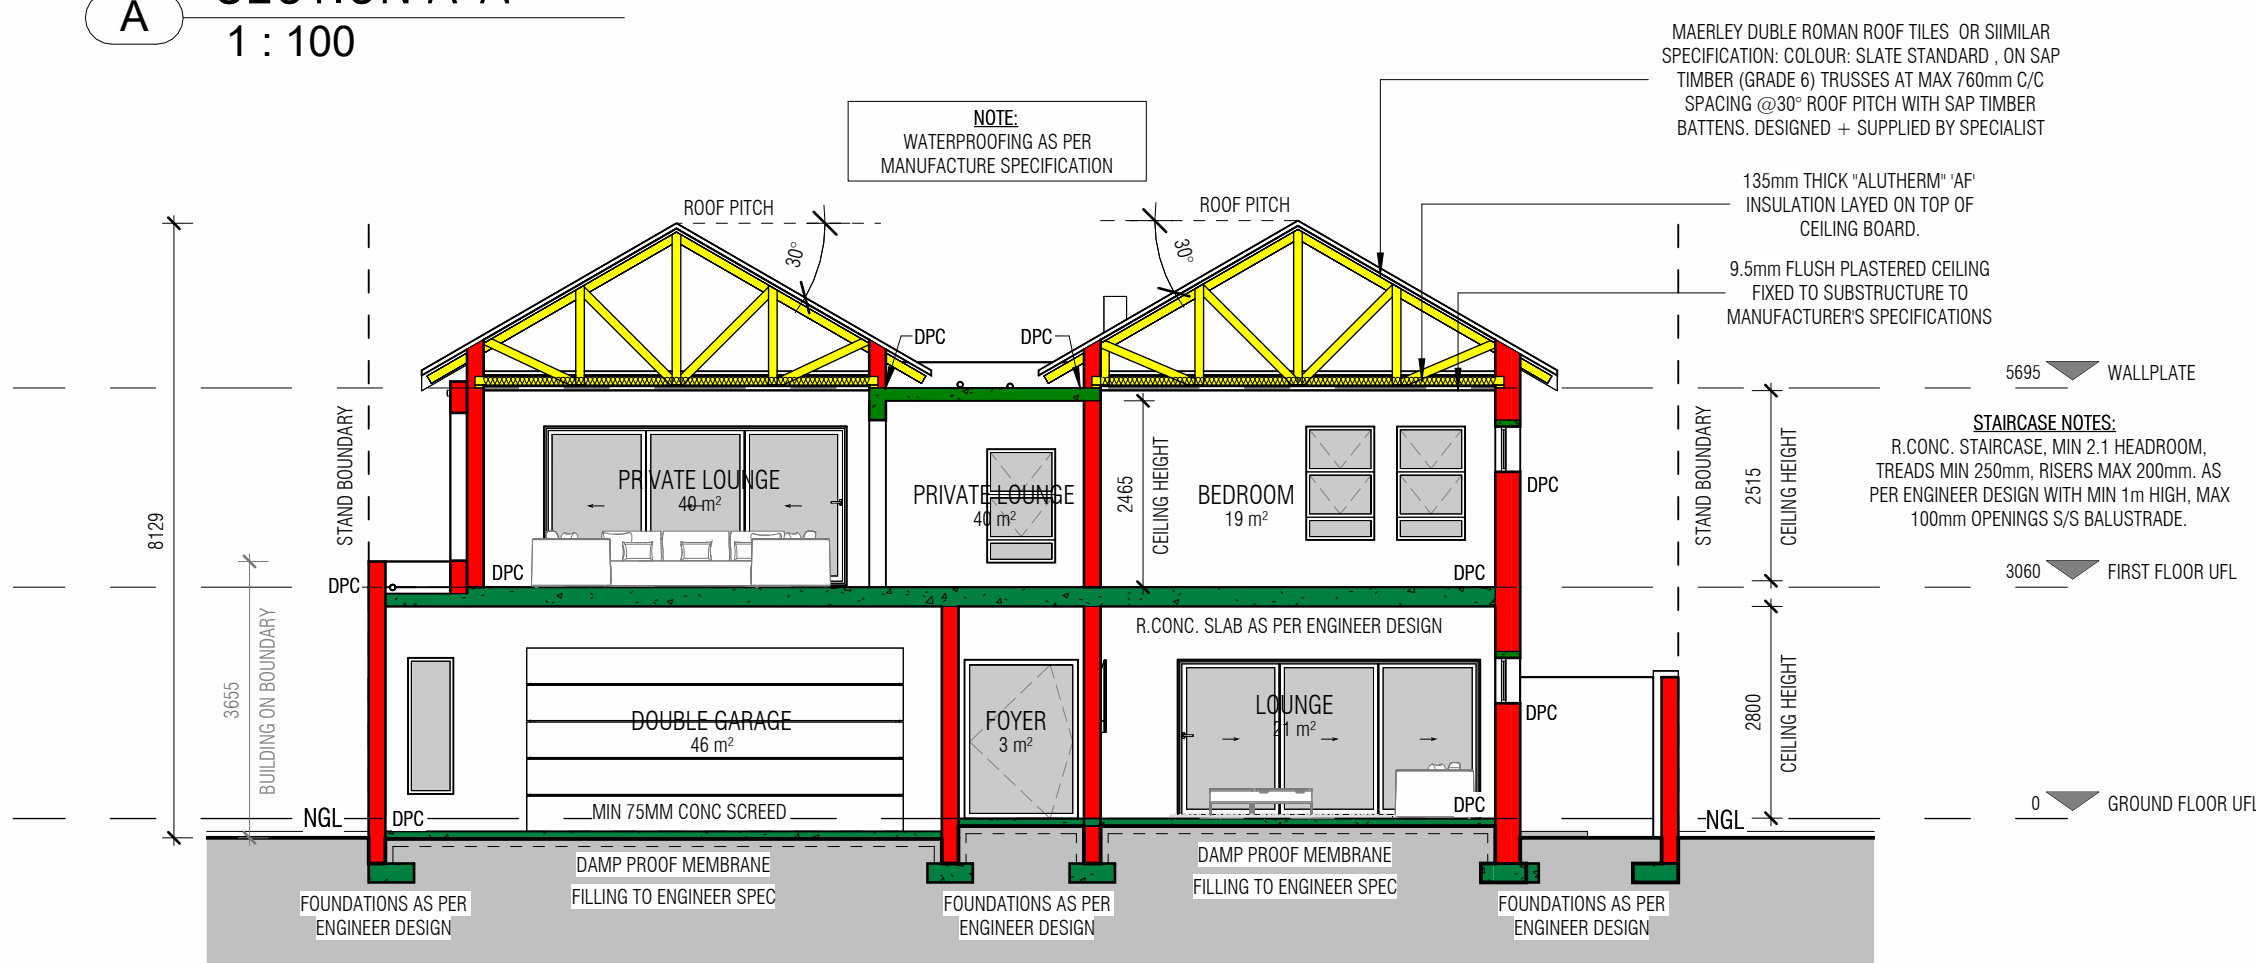

C SECTION C-C
1 : 100



GENERAL NOTES

ALL MEASUREMENTS, HEIGHT AND DESCRIPTIONS MUST BE CHECKED ON THE PLAN BEFORE COMMENCEMENT OF ANY WORK ON SITE. ANY DISCREPANCIES, FAULTS IDENTIFIED, ARE TO BE COMMUNICATED WITH THE ARCHITECT. COPY RIGHTS TO THIS DESIGN AND DRAWING IS RESERVED BY THE ARCHITECT. TAKE NOTE THAT WHERE A SPECIFIC MANUFACTURER'S NAME IS USED THE WORKMANSHIP MUST BE CORRECT TO THE SPECIFICATION OR IF OTHERWISE ALTERATION/DEVIATION TO BE CONSULTED WITH THE ARCHITECT. THE CONTRACTOR/BUILDER TO FAMILIARIZE HIMSELF WITH THE SPECIFICATIONS OF ANY SPECIFIED MANUFACTURER.

SITE LAYOUT

THE CONTRACTOR/BUILDER TO FAMILIARIZE THEMSELVES WITH THE LAYOUT, MEASUREMENTS, AND ALL ADDITIONAL ANNOTATION WITH REGARDS TO THE FOOTPRINT OF THE STRUCTURE ON SITE. ANY ELECTRICAL, SEWERAGE, STORAGE/WATER SUPPLY AND STABILITY ON ALL WORK COMMENCES ON SITE. ANY CHANGED TO SUCH RESERVATIONS ARE THE RESPONSIBILITY OF THE OWNER. THE ENGINEER WILL BE RESPONSIBLE FOR ANY SLABS, LOAD BEARING STRUCTURES AND DEFECTIVE/ SENSITIVE/ IRREGULAR GROUND CONDITIONS

CHIMNEYS AND BRAAIS

VERIFICATION OF CORRECT SIZES TO BE CONSIDERED AS PER MANUFACTURER'S DETAILS. BEFORE ANY CHIMNEY/ BRAAI ARE BUILT, ANY DEVIATION FROM THE PROPOSED STRUCTURES TO DISCUSSED WITH THE ARCHITECT BEFORE HAND.

ELECTRICAL

REFER TO ELECTRICAL PLAN AND MUST BE DISCUSSED WITH CLIENTS BEFORE HAND. INDICATION OF ANY GARDEN LIGHTS AND REMOTE GATE CONTROLS NOT SHOWN ON THE PLAN.

FOUNDATION

FOUNDATION DESIGNS TO COMPLY WITH SANS 10400-B OR THE DETAILED REQUIREMENTS OF SANS 10400-H. RECOMMENDATIONS AND PREFERRED FOUNDATION METHODS TO BE CONFIRMED WITH THE APPOINTED ENGINEER PRIOR TO ANY COMMENCEMENT OF ANY GROUND WORKS.

WALLS

CONSTRUCTION OF WALLS TO COMPLY WITH THE SANS 10400-B & 10400-T. A STANDARD OF 220mm EXTERNAL WALL & 110mm TO BE APPLIED. STRENGTH AND STABILITY ON ALL WALLS ARE REQUIRED IN CONJUNCTION WITH STANDARD BUILDING PRACTICE. WALL FINISHES TO COMPLY WITH THE SPECIFICATIONS ON THE ELEVATIONS.

ROOFS

ROOF COVERING AND WATERPROOFING NEED TO BE IN CONJUNCTIONS WITH THE SANS 10400-L. FLAT ROOFS OR RELATED GUTTERS NEED TO BE IN CONSTRUCTED IN ACCORDANCE WITH THE DETAILED REQUIREMENTS OF SANS 10400-L OR RATIONALLY DESIGNED BY AN APPROVED COMPETENT PERSON. ROOF ASSEMBLY AND CEILING INSTALLATION MUST BE CONSTRUCTED IN ACCORDANCE TO SANS 10400-C AS WELL AS SANS 10400-L & 10400-K OR SANS 10400-T IN TERMS OF THE FIRE RESISTANCE & COMBUSTIBILITY. GUTTERS & DOWNPIPES MUST BE SIZED IN ACCORDANCE WITH SANS-10400-M

WOOD

DRYWALLS TO COMPLY WITH SANS 10082/ WOOD SANS 0163.

LIGHTING AND VENTILATION

CROSS VENTILATION (5%) AND LIGHTING (10%) IN HABITABLE ROOMS. LIGHTING AND VENTILATION IN ANY ROOM SHOULD COMPLY WITH SANS 10400-T AND THE REQUIREMENTS OF SANS 10400-O OR ALTERNATIVELY BE RATIONALLY DESIGNED. MECHANICAL VENTILATION AND ARTIFICIAL LIGHTING TO BE CONSIDERED FOR BASEMENTS AND ROOMS ALIKE.

DRAINAGE

DRAINAGE SYSTEMS TO BE IN ACCORDANCE WITH SANS 10400-P OR ALTERNATIVELY RATIONALLY DESIGNED BY A COMPETENT PERSON.

THE FOLLOWING TO BE CONSIDERED WITH THE INSTALLATION OF THE DRAINAGE SYSTEM:

WC TO BE FITTED TO 110mm DIA uPVC SOIL PIPE
HWS/BATHS/BATHS/SHOWERS
TO BE FITTED TO 50mm DIA uPVC WASTE PIPE

DRAINAGE INVERT LEVEL TO BE A MINIMUM OF 450MM
ALL SOIL PIPES BE INSTALLED USING uPVC 100MM DIA PIPES WITH A STANDARD GRADIENT OF 1:40. THE GRADIENT TO BE CONSIDERED AS PER SLOPE OF FALL ON THE SITE AS PROVISIONS TO BE MADE DEPENDANT ON THE SURFACE

FIRE NOTES

INSTALLATION TO BE DONE ACCORDING TO THE TO THE SANS 10400 - W AND WATER SUPPLY ACCORDING TO SANS 10400-T OR AS PER RATIONAL DESIGN BY COMPETENT PERSON.
-ALL CHIMNEYS AS PER PART "Y" OF NBR
-NO COMBUSTIBLE ROOF ELEMENTS SHALL PENETRATE THE SEPARATING ELEMENTS BETWEEN ANY HABITABLE ROOM AND GARAGE.
-ALL DOORS LEADING TO THE GARAGE TO BE SOLID WOOD STABLE DOORS, FOR FIREPROOF DOOR TYPE.

STORM WATER

IMPLEMENTED ACCORDING TO SANS 10400-R OR RATIONALLY DESIGNED BY AN APPROVED COMPETENT PERSON.

GLAZING

THE TYPE AND FIXING TO BE IN ACCORDANCE WITH SANS 10400-B OR THE DETAILED REQUIREMENTS OF SANS 10400-N. A GLAZING SELECTION TO BE MADE IN ACCORDANCE TO THE DETAILED REQUIREMENTS OF SANS 10400-N. SEE NOTES ON ALL SELECTION ON THE WINDOW SCHEDULE.

GLAZING AS PER "N" OF NBR

STAIR DETAIL

STAIRWAYS TO E CONSTRUCTED IN ACCORDANCE TO THE SANS 10400-B & SANS 10400-T OR DETAILED REQUIREMENTS OF SANS 10400-M. A COMPETENT PERSON TO BE APPOINTED WITH REGARDS TO THE STABILITY AND STRENGTH OF THE STAIRWAYS.
ANY ITEM(S) ACTING AS BALUSTRADES TO THE STAIRS NEED TO COMPLY WITH SANS 10400-B &/OR SANS 10400-K &/OR 10400-T.

STAIRWAY:
TREADS - MIN 250MM
RISERS - MAX 200MM
FLOOR FINISH TO BE CARPET OR SLIP-FREE TILES AS CHOSEN BY CLIENT.

BALUSTRADES:
MIN 1000MM HIGH BALUSTRADES STEEL/GLASS/ALUMINUM AS CHOSEN BY CLIENT.
1000MM SPACING
SPECIFICATION AS PER MANUFACTURER
ENGINEER DETAILS ELSEWHERE.

PROJECT TITLE

PROPOSED NEW DWELLING FOR:
SS DE BEER
ON STAND : 1103 EERSTERUST X02

OWNERS NAME

SS DE BEER

OWNERS SIGNATURE

ENGINEER NAME AND No:

KLK

ENGINEER SIGNATURE:

PREPARED BY:

LJW

ARCHITECT:

LJW

SACAP REG:

CAD545855565

SACAP REG:

5838

SIGNATURE:

SIGNATURE:



DRAWING TITLE:
ELEVATIONS, SECTIONS & 3D VIEWS

DATE:

08/11/23

SCALE:

1 : 100

SHEET SIZE:

A1

PROJECT No:

2023-D014


DRAWING No:

100

REVISION No:

DOOR SCHEDULE


D1				HAND	D2				HAND	D3				HAND	D4				HAND
QUANTITY: 1				LH RH	QUANTITY: 1				LH RH	QUANTITY: 2				LH RH	QUANTITY: 10				LH RH
				1					1					2				4	6
2465					2465					2465					2465				
2125					2125					2125					2125				
UFL					UFL					UFL					UFL				
DOOR	CUSTOM ALUMINUM FRAMED GLASS PIVOT DOOR.				DOOR	MEDIUM DUTY HORIZONTAL SLATTED EXTERNAL TIMBER DOOR.				DOOR	HORIZONTAL SLATED VENEERED CLASS B FIRE DOOR.				DOOR	HORIZONTAL SLATED INTERNAL HOLLOW CORE DOOR.			
DOOR FINISH	POWDER COATED ALUMINUM. MATT CHARCOAL.				DOOR FINISH	2 COATS TIMBER PRESERVATIVE. SAMPLE TO CLIENT/ DESIGNERS APPROVAL.				DOOR FINISH	2 COATS TIMBER PRESERVATIVE. SAMPLE TO CLIENT/ DESIGNERS APPROVAL.				DOOR FINISH	2 COATS TIMBER PRESERVATIVE. SAMPLE TO CLIENT/ DESIGNERS APPROVAL.			
FRAME	SINGLE GLAZED ALUMINUM				FRAME	PRESSED STEEL.				FRAME	PRESSED STEEL.				FRAME	MERANTI			
FRAME FINISH	POWDER COATED ALUMINUM. MATT CHARCOAL.				FRAME FINISH	PRIMED AND PAINTED WITH MIN 2 COATS SATIN ENAMEL. COLOUR AS PER CLIENT/ DESIGNERS APPROVAL.				FRAME FINISH	PRIMED AND PAINTED WITH MIN 2 COATS SATIN ENAMEL. COLOUR AS PER CLIENT/ DESIGNERS APPROVAL.				FRAME FINISH	2 COATS TIMBER PRESERVATIVE. SAMPLE TO CLIENT/ DESIGNERS APPROVAL.			
GLAZING	SINGLE GLAZED LOW 'E' COATED (NON-REFLECTIVE) GLASS WITH MAX.				GLAZING	N/A				GLAZING	N/A				GLAZING	N/A			
DOOR ACCESSORIES	DOOR LOCKSET AND HINGES AS PER CLIENT CHOICE. ALL TO BE INSTALLED AS MANUFACTURER SPEC.				DOOR ACCESSORIES	DOOR LOCKSET AND HINGES AS PER CLIENT CHOICE. ALL TO BE INSTALLED AS MANUFACTURER SPEC.				DOOR ACCESSORIES	DOOR LOCKSET AND HINGES AS PER CLIENT CHOICE. ALL TO BE INSTALLED AS MANUFACTURER SPEC.				DOOR ACCESSORIES	DOOR LOCKSET AND HINGES AS PER CLIENT CHOICE. ALL TO BE INSTALLED AS MANUFACTURER SPEC.			
D5				HAND	FD1				HAND	GG1				HAND	GD1				HAND
QUANTITY: 1				LH RH	QUANTITY: 2				LH RH	QUANTITY: 2				LH RH	QUANTITY: 1				LH RH
				1					1					1					1
2465					2465					2125					2465				
2125					2125					2125					2125				
UFL					UFL					UFL					UFL				
DOOR	HORIZONTAL SLATED INTERNAL HOLLOW CORE DOOR.				DOOR	ALUMINUM FOLDING DOOR, CENTER OPENING.				DOOR	STEEL FRAMED WITH HORIZONTAL STEEL SLATS GARDEN GATE, OPENING OUT.				DOOR	HORIZONTAL SLATTED TIMBER GARAGE DOOR.			
DOOR FINISH	2 COATS TIMBER PRESERVATIVE. SAMPLE TO CLIENT/ DESIGNERS APPROVAL.				DOOR FINISH	POWDER COATED ALUMINUM. BRONZE.				DOOR FINISH	PRIMED AND PAINTED WITH SATIN ENAMEL. COLOUR: CHARCOAL.				DOOR FINISH	2 COATS TIMBER PRESERVATIVE. SAMPLE TO CLIENT/ DESIGNERS APPROVAL.			
FRAME	MERANTI				FRAME	SINGLE GLAZED ALUMINUM				FRAME	50x50 SHS				FRAME	N/A			
FRAME FINISH	2 COATS TIMBER PRESERVATIVE. SAMPLE TO CLIENT/ DESIGNERS APPROVAL.				FRAME FINISH	POWDER COATED ALUMINUM. BRONZE.				FRAME FINISH	PRIMED AND PAINTED WITH SATIN ENAMEL. COLOUR: CHARCOAL.				FRAME FINISH	N/A			
GLAZING	N/A				GLAZING	SINGLE GLAZED LOW 'E' COATED (NON-REFLECTIVE) GLASS WITH MAX.				GLAZING	N/A				GLAZING	N/A			
DOOR ACCESSORIES	DOOR LOCKSET AND HINGES AS PER CLIENT CHOICE. ALL TO BE INSTALLED AS MANUFACTURER SPEC.				DOOR ACCESSORIES	FOLDING DOOR GEAR AS SUPPLIED BY SPECIALIST				DOOR ACCESSORIES	MILD STEEL LOCK BOX WELDED TO FRAME, PRIMED AND PAINTED. 250mm GATE SPRING AS AUTO CLOSER. 127mm GALVANIZED AUTO GATE LATCH.				DOOR ACCESSORIES	AUTOMATED GARAGE DOOR OPENER. ALL OTHER HARDWARE AS SUPPLIED BY MANUFACTURE			

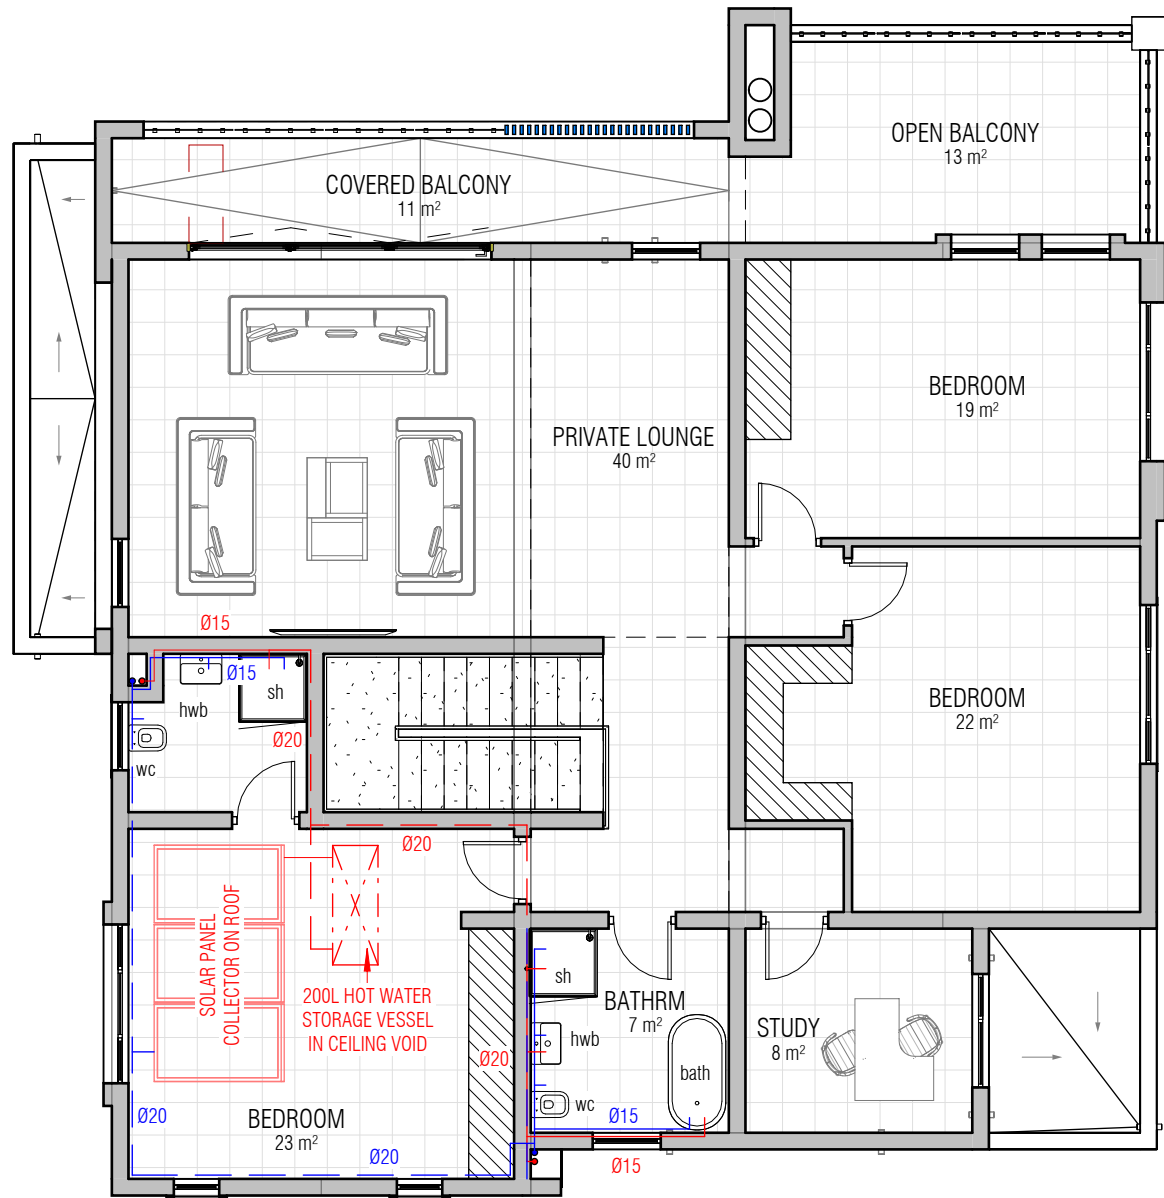

2 FF - WATER RETICULATION LAYOUT
1 : 100

W1	QUANTITY: 2	W2	QUANTITY: 1	W3	QUANTITY: 3	W4	QUANTITY: 1	W5	QUANTITY: 1
WINDOW LEVEL - 2125		WINDOW LEVEL - 2125		WINDOW LEVEL - 2125		WINDOW LEVEL - 2125		WINDOW LEVEL - 2125	
UFL		UFL		UFL		UFL		UFL	
WINDOW DESCRIPTION	ALUMINUM WINDOW WITH TOP HUNG OPENING SECTION AND FIXED	WINDOW DESCRIPTION	ALUMINUM WINDOW WITH TOP HUNG OPENING SECTION AND FIXED	WINDOW DESCRIPTION	ALUMINUM WINDOW WITH TOP HUNG OPENING SECTION AND FIXED	WINDOW DESCRIPTION	ALUMINUM WINDOW WITH TOP HUNG OPENING SECTION AND FIXED	WINDOW DESCRIPTION	ALUMINUM WINDOW WITH TOP HUNG OPENING SECTION AND FIXED
FRAME	ALUMINUM	FRAME	ALUMINUM	FRAME	ALUMINUM	FRAME	ALUMINUM	FRAME	ALUMINUM
FRAME FINISH	BLACK, POWDER COATED	FRAME FINISH	BLACK, POWDER COATED	FRAME FINISH	BLACK, POWDER COATED	FRAME FINISH	BLACK, POWDER COATED	FRAME FINISH	BLACK, POWDER COATED
GLAZING	SINGLE GLAZED LOW 'E' COATED GLASS WITH MAX. U VALUE OF 4.3W/m²·K (STANDARD: SANS 204:2011)	GLAZING	SINGLE GLAZED LOW 'E' COATED GLASS WITH MAX. U VALUE OF 4.3W/m²·K (STANDARD: SANS 204:2011)	GLAZING	SINGLE GLAZED LOW 'E' COATED GLASS WITH MAX. U VALUE OF 4.3W/m²·K (STANDARD: SANS 204:2011)	GLAZING	SINGLE GLAZED LOW 'E' COATED GLASS WITH MAX. U VALUE OF 4.3W/m²·K (STANDARD: SANS 204:2011)	GLAZING	SINGLE GLAZED LOW 'E' COATED GLASS WITH MAX. U VALUE OF 4.3W/m²·K (STANDARD: SANS 204:2011)
W6	QUANTITY: 1	W7	QUANTITY: 4	W8	QUANTITY: 4	W9	QUANTITY: 4	CW1	QUANTITY: 1
WINDOW LEVEL - 2125		WINDOW LEVEL - 2125		WINDOW LEVEL - 2125		WINDOW LEVEL - 2125		WINDOW LEVEL - 2125	
UFL		UFL		UFL		UFL		UFL	
WINDOW DESCRIPTION	ALUMINUM WINDOW WITH TOP HUNG OPENING SECTION AND FIXED	WINDOW DESCRIPTION	ALUMINUM WINDOW WITH TOP HUNG OPENING SECTION AND FIXED	WINDOW DESCRIPTION	ALUMINUM WINDOW WITH TOP HUNG OPENING SECTION AND FIXED	WINDOW DESCRIPTION	ALUMINUM WINDOW WITH TOP HUNG OPENING SECTION AND FIXED	WINDOW DESCRIPTION	ALUMINUM WINDOW WITH FIXED PANEL SECTIONS AS INDICATED
FRAME	ALUMINUM	FRAME	ALUMINUM	FRAME	ALUMINUM	FRAME	ALUMINUM	FRAME	ALUMINUM
FRAME FINISH	BLACK, POWDER COATED	FRAME FINISH	BLACK, POWDER COATED	FRAME FINISH	BLACK, POWDER COATED	FRAME FINISH	BLACK, POWDER COATED	FRAME FINISH	BLACK, POWDER COATED
GLAZING	SINGLE GLAZED LOW 'E' COATED GLASS WITH MAX. U VALUE OF 4.3W/m²·K (STANDARD: SANS 204:2011)	GLAZING	SINGLE GLAZED LOW 'E' COATED GLASS WITH MAX. U VALUE OF 4.3W/m²·K (STANDARD: SANS 204:2011)	GLAZING	SINGLE GLAZED LOW 'E' COATED GLASS WITH MAX. U VALUE OF 4.3W/m²·K (STANDARD: SANS 204:2011)	GLAZING	SINGLE GLAZED LOW 'E' COATED GLASS WITH MAX. U VALUE OF 4.3W/m²·K (STANDARD: SANS 204:2011)	GLAZING	SINGLE GLAZED LOW 'E' COATED GLASS WITH MAX. U VALUE OF 4.3W/m²·K (STANDARD: SANS 204:2011)

GLAZING SCHEDULE

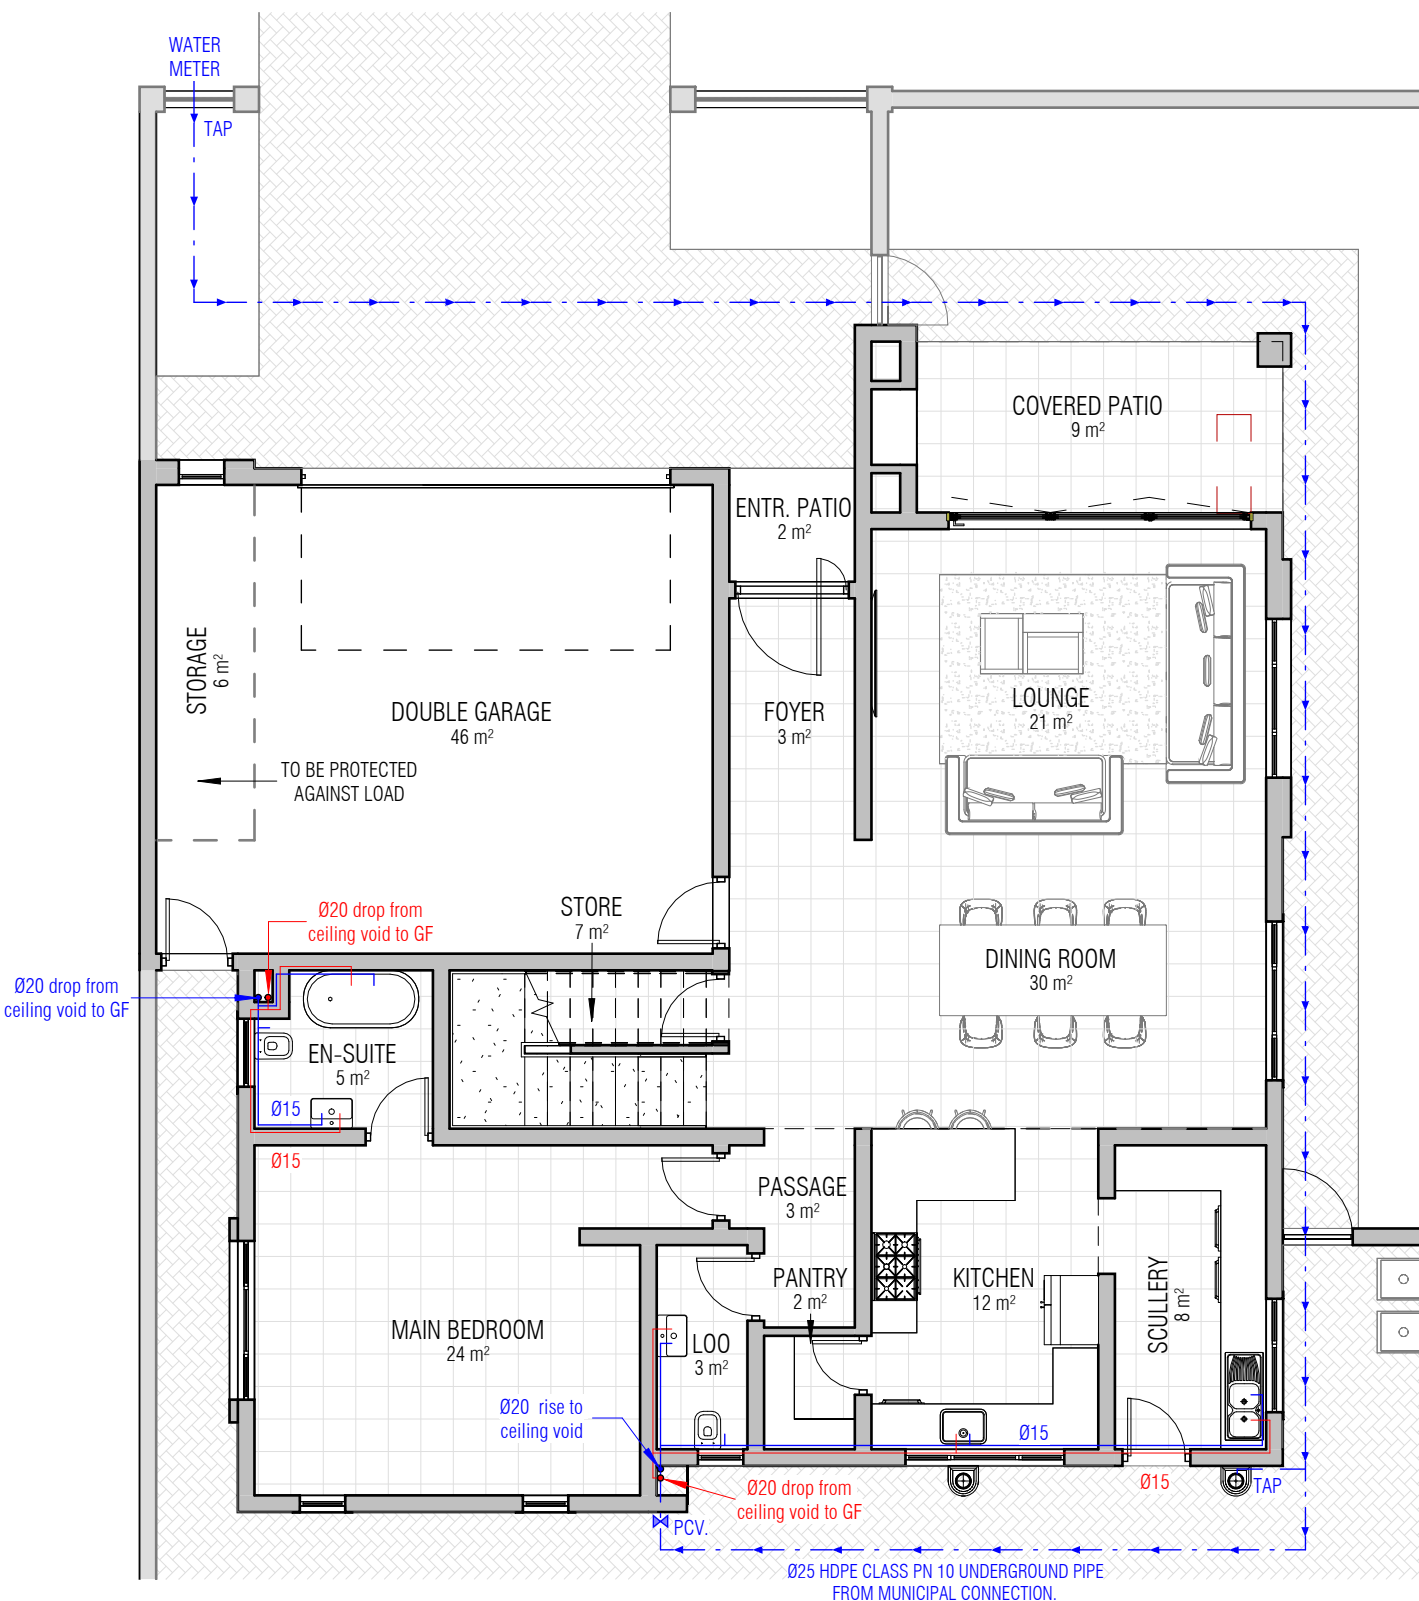

1 GF - WATER RETICULATION LAYOUT
1 : 100

GENERAL NOTES

ALL MEASUREMENTS, HEIGHT AND DESCRIPTIONS MUST BE CHECKED ON THE PLAN BEFORE COMMENCEMENT OF ANY WORK ON SITE. ANY DISCREPANCIES, FAULTS IDENTIFIED, ARE TO BE COMMUNICATED WITH THE ARCHITECT. COPY RIGHTS TO THIS DESIGN AND DRAWING IS RESERVED BY THE ARCHITECT. TAKE NOTE THAT WHERE A SPECIFIC MANUFACTURERS NAME IS USED THE WORKMANSHIP MUST BE CORRECT TO THE SPECIFICATION OR IF OTHERWISE ALTERATION/DEVIATION TO BE CONSULTED WITH THE ARCHITECT. THE CONTRACTOR/BUILDER TO FAMILIARIZE HIMSELF WITH THE SPECIFICATIONS OF ANY SPECIFIED MANUFACTURER.

SITE LAYOUT

THE CONTRACTOR/BUILDER TO FAMILIARIZE THEMSELVES WITH THE LAYOUT, MEASUREMENTS, AND ALL ADDITIONAL ANNOTATION WITH REGARDS TO THE FOOTPRINT OF THE STRUCTURE ON SITE. ANY ELECTRICAL, SEWERAGE, STORMWATER SERVITUDE TO BE CONSIDERED BEFORE ANY WORK COMMENCES ON SITE. ANY CHANGED TO SUCH RESERVATIONS ARE THE RESPONSIBILITY OF THE OWNER. THE ENGINEER WILL BE RESPONSIBLE FOR ANY SLABS, LOAD BEARING STRUCTURES AND DEFECTIVE/ SENSITIVE/ IRREGULAR GROUND CONDITIONS

CHIMNEYS AND BRAAIS

VERIFICATION OF CORRECT SIZES TO BE CONSIDERED AS PER MANUFACTURES DETAILS. BEFORE ANY CHIMNEY/ BRAAI ARE BUILT, ANY DEVIATION FROM THE PROPOSED STRUCTURES TO DISCUSSED WITH THE ARCHITECT BEFORE HAND.

ELECTRICAL

REFER TO ELECTRICAL PLAN AND MUST BE DISCUSSED WITH CLIENTS BEFORE HAND. INDICATION OF ANY GARDEN LIGHTS AND REMOTE GATE CONTROLS NOT SHOWN ON THE PLAN.

FOUNDATION

FOUNDATION DESIGNS TO COMPLY WITH SANS 10400-B OR THE DETAILED REQUIREMENTS OF SANS 10400-H. RECOMMENDATIONS AND PREPARED FOUNDATION METHODS TO BE CONFIRMED WITH THE APPOINTED ENGINEER PRIOR TO ANY COMMENCEMENT OF ANY GROUND WORKS.

WALLS

CONSTRUCTION OF WALLS TO COMPLY WITH THE SANS 10400-B & 10400-T. A STANDARD OF 220mm EXTERNAL WALL & 110mm TO BE APPLIED. STRENGTH AND STABILITY ON ALL WALLS ARE REQUIRED IN CONJUNCTION WITH STANDARD BUILDING PRACTICE. WALL FINISHES TO COMPLY WITH THE SPECIFICATIONS ON THE ELEVATIONS.

ROOFS

ROOF COVERING AND WATERPROOFING NEED TO BE IN CONJUNCTIONS WITH THE SANS 10400-L. FLAT ROOFS OR RELATED GUTTERS NEED TO BE IN CONSTRUCTED IN ACCORDANCE WITH THE DETAILED REQUIREMENTS OF SANS 10400-L OR RATIONALLY DESIGNED BY AN APPROVED COMPETENT PERSON. ROOF ASSEMBLY AND CEILING INSTALLATION MUST BE CONSTRUCTED IN ACCORDANCE TO SANS 10400-C AS WELL AS SANS 10400-L & 10400-K OR SANS 10400-T IN TERMS OF THE FIRE RESISTANCE & COMBUSTIBILITY. GUTTERS & DOWNPIPES MUST BE SIZED IN ACCORDANCE WITH SANS-10400-M

WOOD

DRYWALLS TO COMPLY WITH SANS 10082/ WOOD SANS 0163.

LIGHTING AND VENTILATION

CROSS VENTILATION (5%) AND LIGHTING (10%) IN HABITABLE ROOMS. LIGHTING AND VENTILATION IN ANY ROOM SHOULD COMPLY WITH SANS 10400-T AND THE REQUIREMENTS OF SANS 10400-O OR ALTERNATIVELY TO BE RATIONALLY DESIGNED. MECHANICAL VENTILATION AND ARTIFICIAL LIGHTING TO BE CONSIDERED FOR BASEMENTS AND ROOMS ALIKE.

DRAINAGE

DRAINAGE SYSTEMS TO BE IN ACCORDANCE WITH SANS 10400-P OR ALTERNATIVELY RATIONALLY DESIGNED BY A COMPETENT PERSON.

THE FOLLOWING TO BE CONSIDERED WITH THE INSTALLATION OF THE DRAINAGE SYSTEM:

-WC TO BE FITTED TO 110mm DIA uPVC SOIL PIPE

-HWS/SHW/BATHS/SHOWERS TO BE FITTED TO 50mm DIA uPVC WASTE PIPE

DRAINAGE INVERT LEVEL TO BE A MINIMUM OF 450MM. ALL SOIL PIPES BE INSTALLED USING uPVC 100MM DIA PIPES WITH A STANDARD GRADIENT OF 1:40. THE GRADIENT TO BE CONSIDERED AS PER SLOPE OF FALL ON THE SITE AS PROVISIONS TO BE MADE DEPENDANT ON THE SURFACE

FIRE NOTES

INSTALLATION TO BE DONE ACCORDING TO THE TO THE SANS 10400 - W AND WATER SUPPLY ACCORDING TO SANS 10400-T OR AS PER RATIONAL DESIGN BY COMPETENT PERSON. ALL CHIMNEYS AS PER PART 'Y' OF NBR -NO COMBUSTIBLE ROOF ELEMENTS SHALL PENETRATE THE SEPARATING ELEMENTS BETWEEN ANY HABITABLE ROOM AND GARAGE. -ALL DOORS LEADING TO THE GARAGE TO BE SOLID WOOD STABLE DOORS, FOR FIREPROOF DOOR TYPE.

STORM WATER

IMPLEMENTED ACCORDING TO SANS 10400-R OR RATIONALLY DESIGNED BY AN APPROVED COMPETENT PERSON.

GLAZING

THE TYPE AND FINING TO BE IN ACCORDANCE WITH SANS 10400-B OR THE DETAILED REQUIREMENTS OF SANS 10400-N. GLAZING SELECTION TO BE MADE IN ACCORDANCE TO THE DETAILED REQUIREMENTS OF SANS 10400-N. SEE NOTES ON ALL SELECTION ON THE WINDOW SCHEDULE.

-GLAZING AS PER 'N' OF NBR

STAIR DETAIL

STAIRWAYS TO E CONSTRUCTED IN ACCORDANCE TO THE SANS 10400-B & SANS 10400-T OR DETAILED REQUIREMENTS OF SANS 10400-M. A COMPETENT PERSON TO BE APPOINTED WITH REGARDS TO THE STABILITY AND STRENGTH OF THE STAIRWAYS. ANY ITEM(S) ACTING AS BALUSTRADES TO THE STAIRS NEED TO COMPLY WITH SANS 10400-B &/OR SANS 10400-K &/OR 10400-T.

STAIRWAY: TREADS - MIN 250MM RISES - MAX 200MM FLOOR FINISH TO BE CARPET OR SLIP-FREE TILES AS CHOSEN BY CLIENT.

BALUSTRADES: MIN 1000MM HIGH BALUSTRADES STEEL/GLASS/ALUMINUM AS CHOSEN BY CLIENT. -100MM SPACING. SPECIFICATION AS PER MANUFACTURER. ENGINEER DETAILS ELSEWHERE.

PROJECT TITLE

PROPOSED NEW DWELLING FOR:
SS DE BEER
ON STAND : 1103 EERSTERUST X02

OWNERS NAME SS DE BEER

OWNERS SIGNATURE

ENGINEER NAME AND No: ENGINEER SIGNATURE:

PREPARED BY: KLK ARCHITECT: LJW

SACAP REG: CAD54585565 SACAP REG: 5838

SIGNATURE: SIGNATURE:

SIGNATURE: SIGNATURE:

